

POOL SYMBOL LEGEND

- R

Pool Returns
- AF

Auto Fill Line
- SK

Skimmer
- B

Bubblers
- PC

Pool Cleaner
- M

Main Drains
- L

Pool Lights
- U

Umbrella Holder
- D

Pool Drains
- 3" Pool Suction
- 2" Pool Returns
- 2" Skimmers
- 2" Bubblers
- Auto Fill Line
- 1" Light Conduit
- 2 Way 2"-2 1/2" Diverter Valve
- 3 Way 2"-2 1/2" Diverter Valve
- Check Valve
- Hayward 2" Skimmer with Drain Line




32" Aquastar Channel Drains

FEATURES

Unblockable!
Improved water stop and sump design

32" Water Stop and Sump Design

32" Water Stop and Sump Design

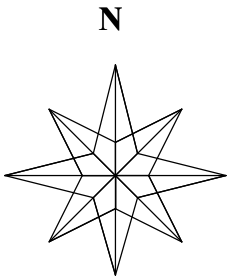
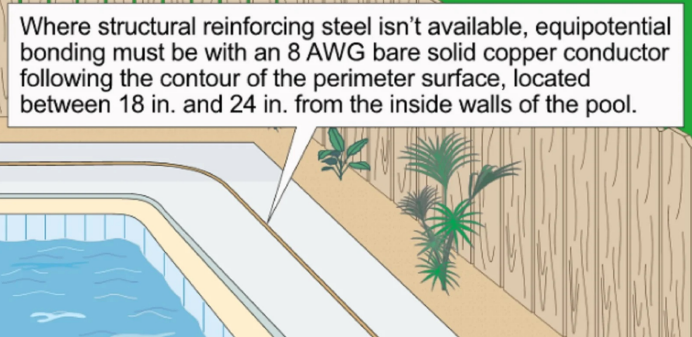
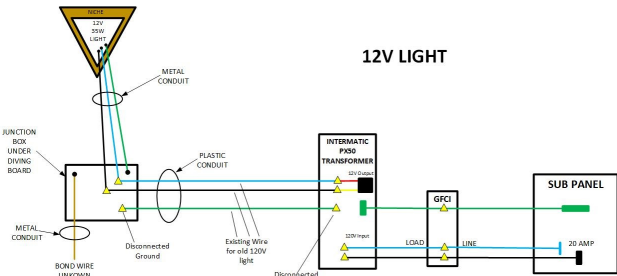


Pool Specifications	
Envelope:	40' x 20'
Perimeter:	120'
Area:	800 ft²
Int Surface Area:	1367.37 ft²
Depth:	3' 6" to 5' 3" to 7'
Volume:	22,705 gallons
32" Aquastar Channel Drains :	1
Skimmers:	2
Led Custom Pool Lights:	4
Pool Returns:	4
Interior Finish:	Mini Pebble
Tile Material:	Custom
Pool Cleaner Line:	1
Coping Material:	Travertine Coping
Step Linear Ft:	59'
Custom Sunshelf:	20' X 10'
Excavation - Hole:	4172 ft³
Concrete:	42.7 yards³
Rebar:	3535' 10"


Hardscapes Specifications	
Total Area:	1085 ft² Pus the Existing Patio and Stepper Pads
Surface Material:	Travertine Decking
Deck Drain:	TBD
Deck Drain Type:	TBD
Coping Material:	Travertine Coping

Pool Equipment	
Circ Pumps:	1 - Hayward Tristar 2.7 HP VS 950
Filters:	1 - Hayward 425 Cartridge Filter Swimclear
Heaters:	1- Hayward 140K Heatpro Heat & Chill Electric
Control Automation System:	1- Hayward Omni PL 4
Wifi Smart Control:	1 - Hayward Wifi Smart app Link
Robot Cleaner:	TBD
Sanitizer:	1 - Hayward Aquarite Salt Generator 40K
Pool Lights:	4 - Hayward Led Color Lgic Lights
Hayward 3 Way -2"-2.5" Diverter Valve:	2
Hayward 2 Way 2"-2.5" Diverter Valve:	8
Hayward 1.5" - 2" Check Valve:	0
Hayward Actuator Valves:	2
Hayward Auto Water Fill System:	Yes
Child Safety Alarms:	TBD
Child Safety Fence:	TBD
Deluxe Pool Cleaning Maintenace Kit:	Yes
Other:	3 - Led Color Bubblers, 1 - Umbrella Holder
Other:	Sunken Fire-Pit, Basketball Court, Cabana
Other:	

Project Info	
Project Name:	Keydrick Vincent
Client Email:	k.vincent08@yahoo.com
Client Phone:	407-982-0691
Address:	Lot 10: Oxford Preserve Trl
City:	Oxford
State/Province:	FL
Zip/Postal Code:	34484
Description:	Custom Pool Plans
Designer Name:	Kayne Marzetti
Company Name:	Pool Design Consultant

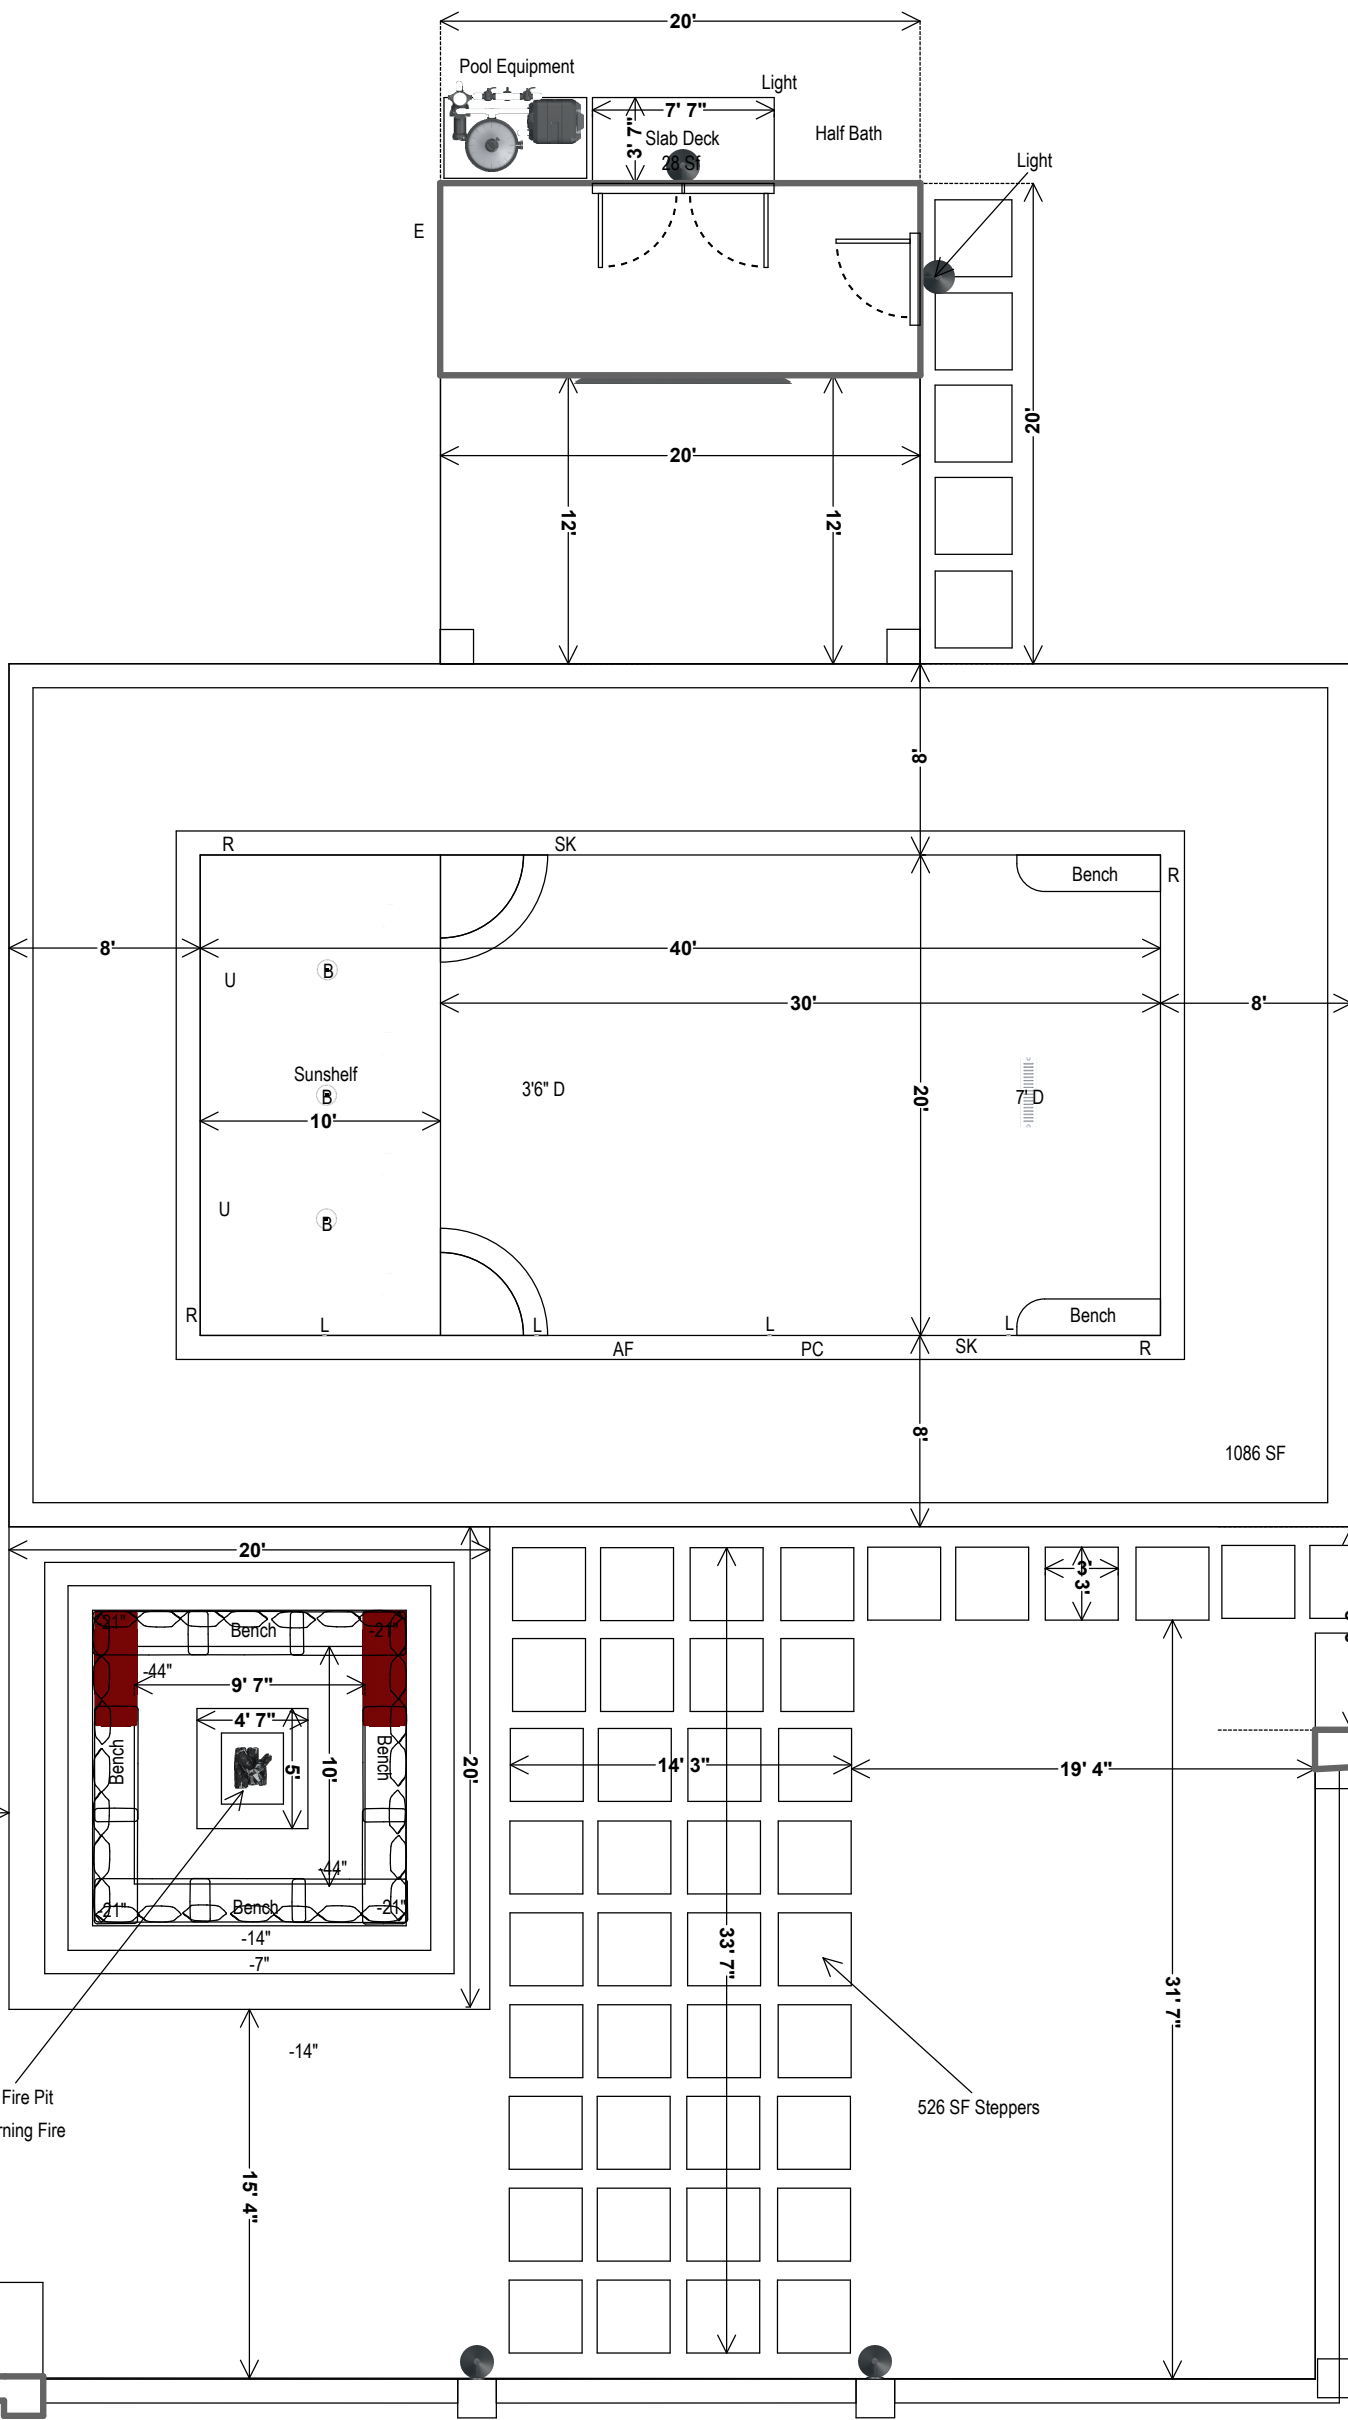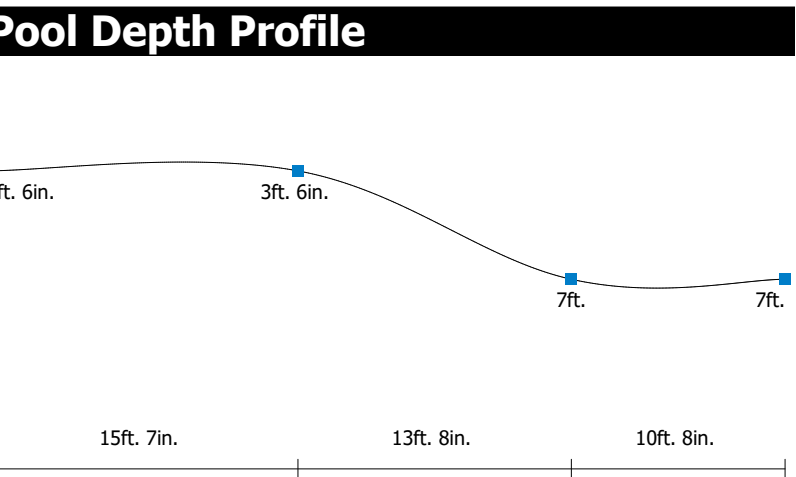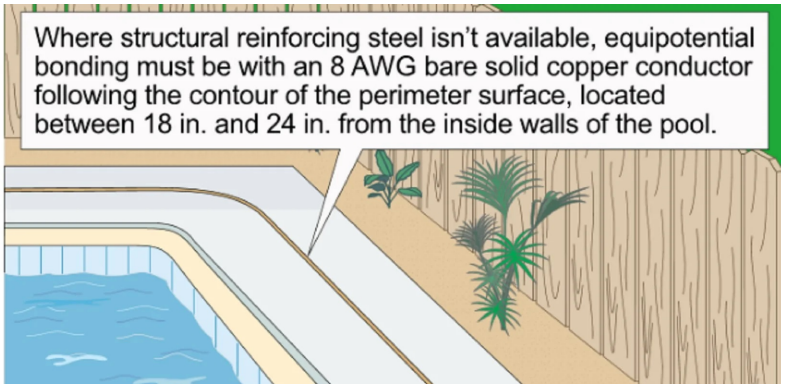

TRISTAR VS 950 DIMENSIONS (INCHES)

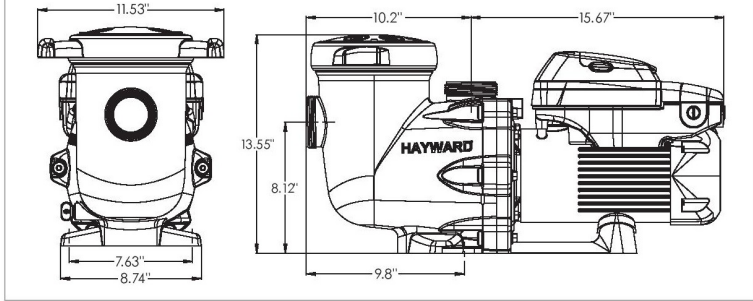


Tristar VS 950 pumps are listed by NSF

**When sold by a Totally Hayward® partner. Exclusions, other terms and conditions may apply — visit hayward.com/expert for details.

* hayward.com * 1-888-HAYWARD

TRISTAR VS 950 PERFORMANCE COMPARISON

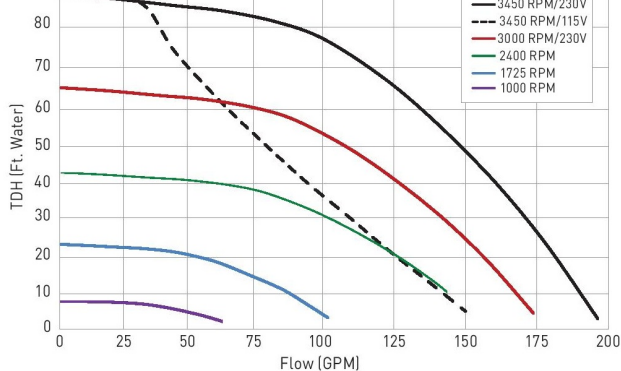

Scale: 1/8" = 1 ft